
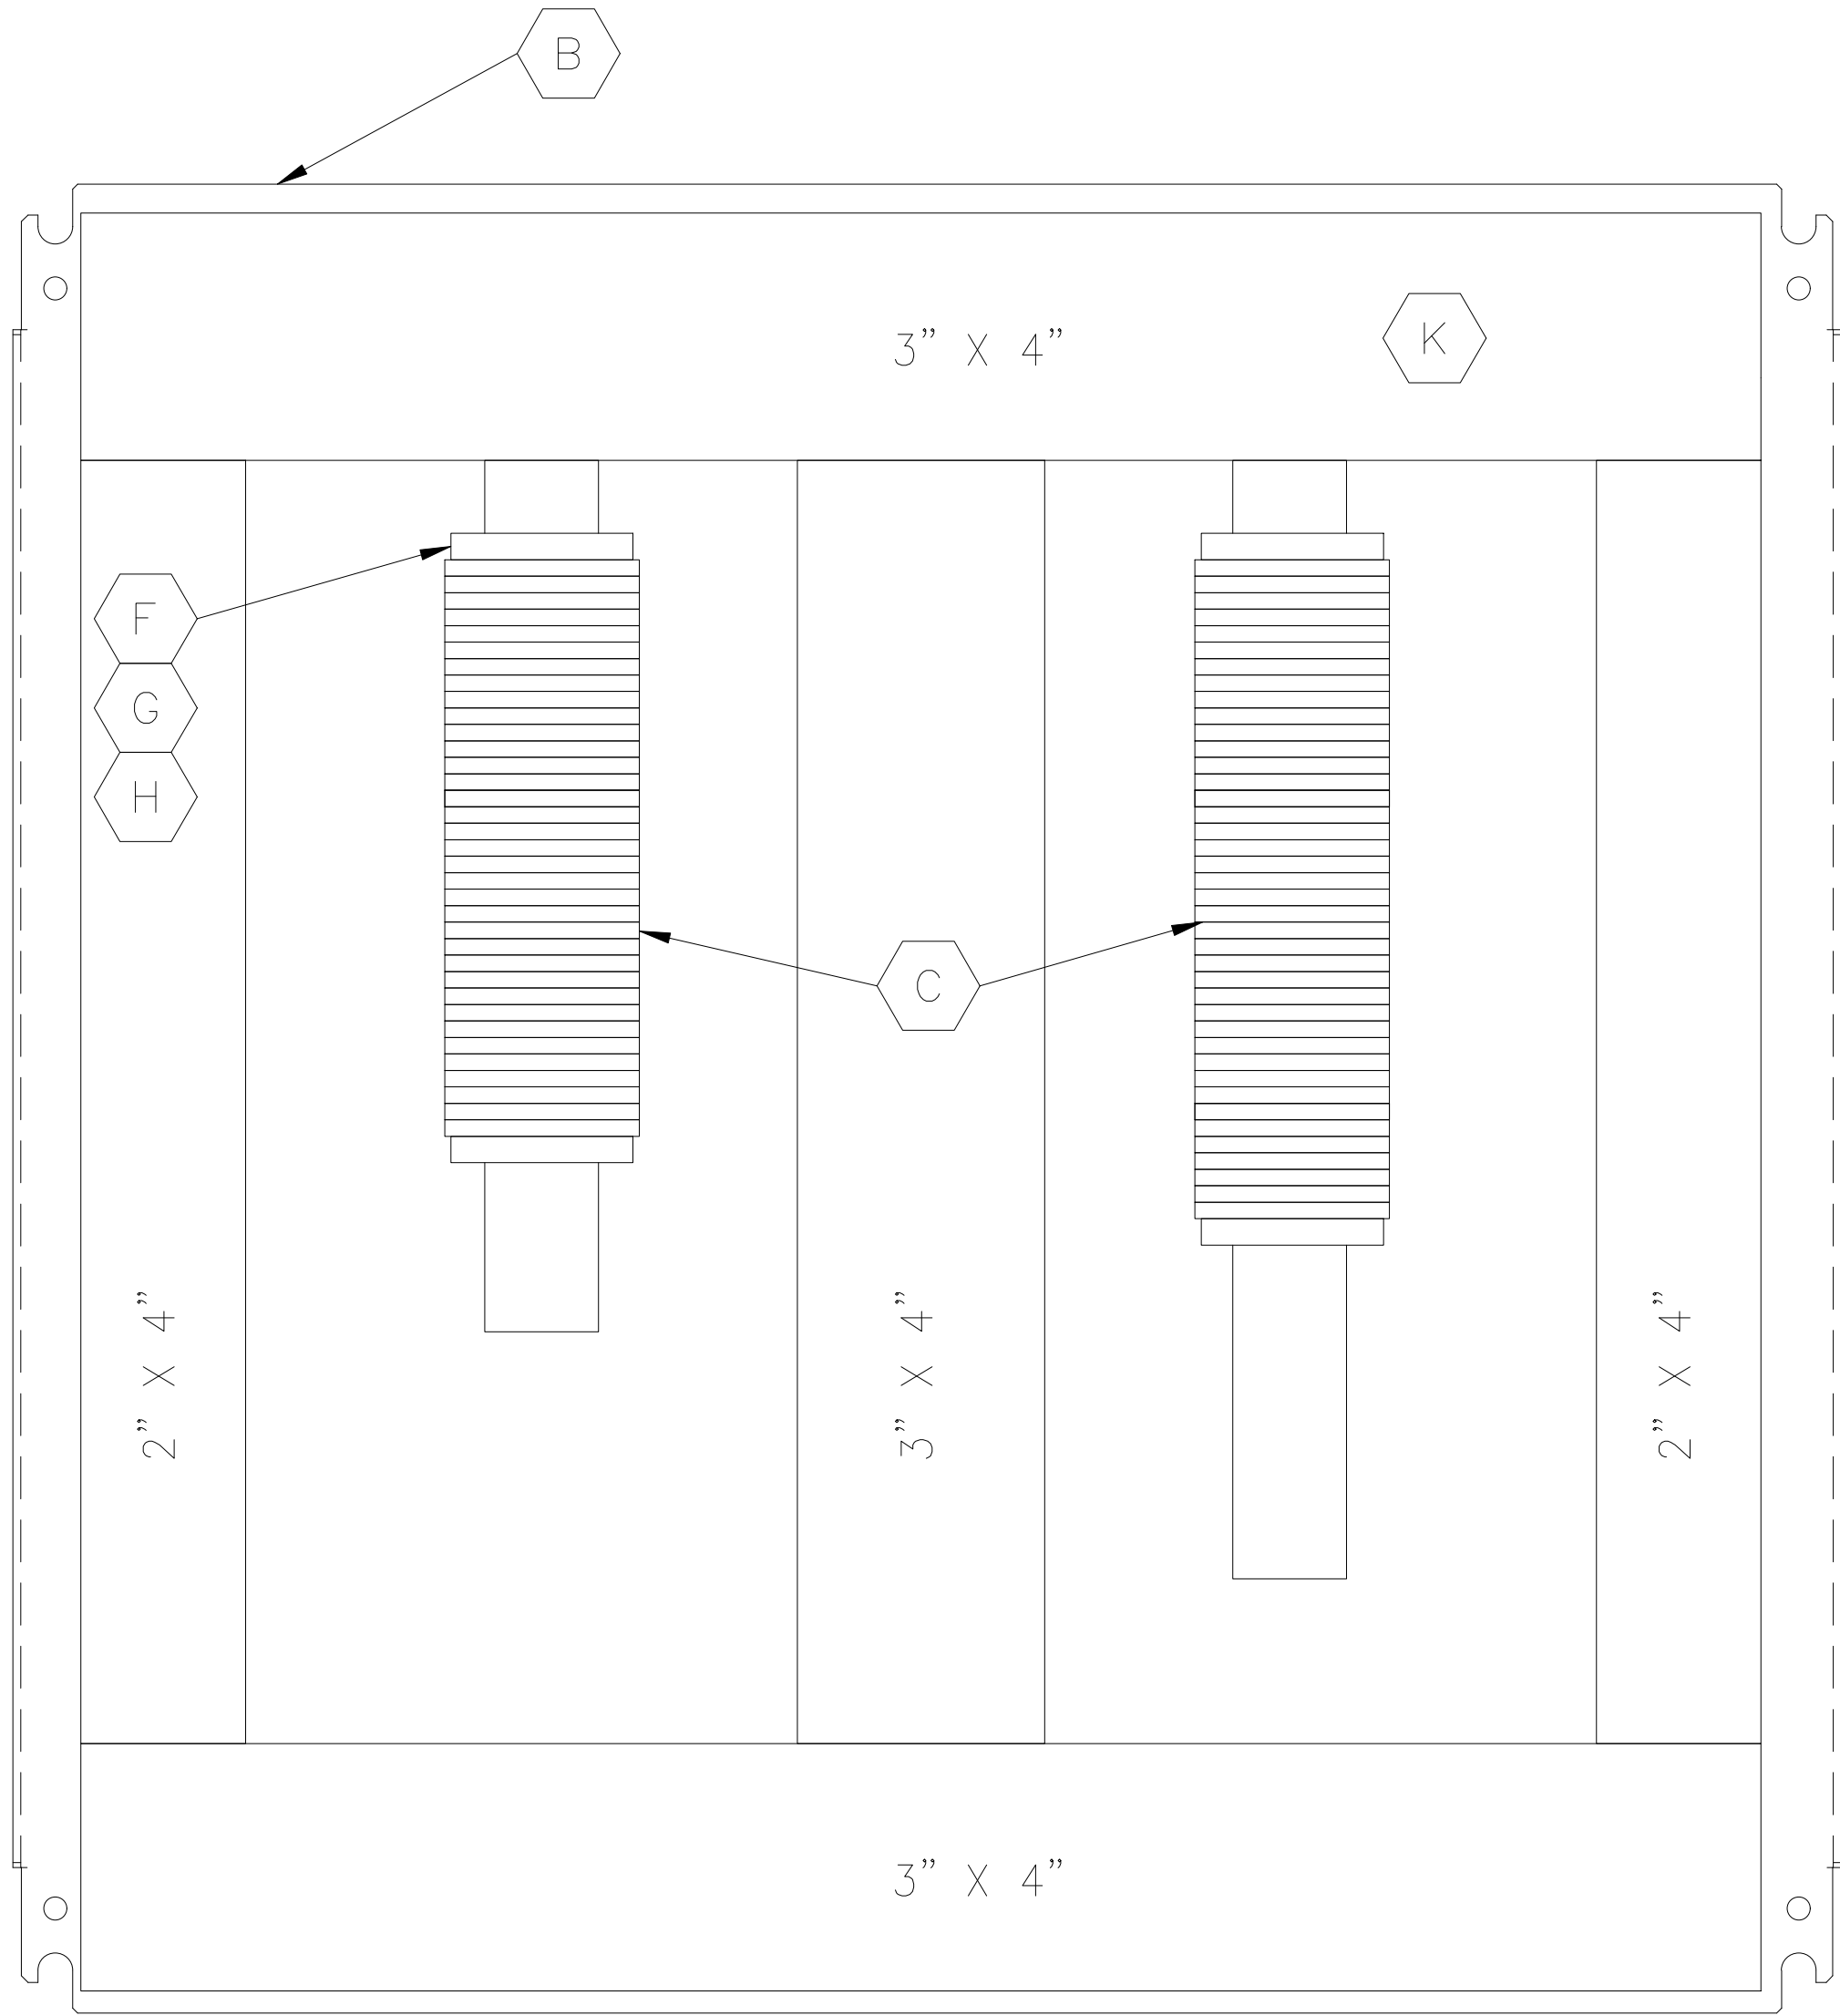


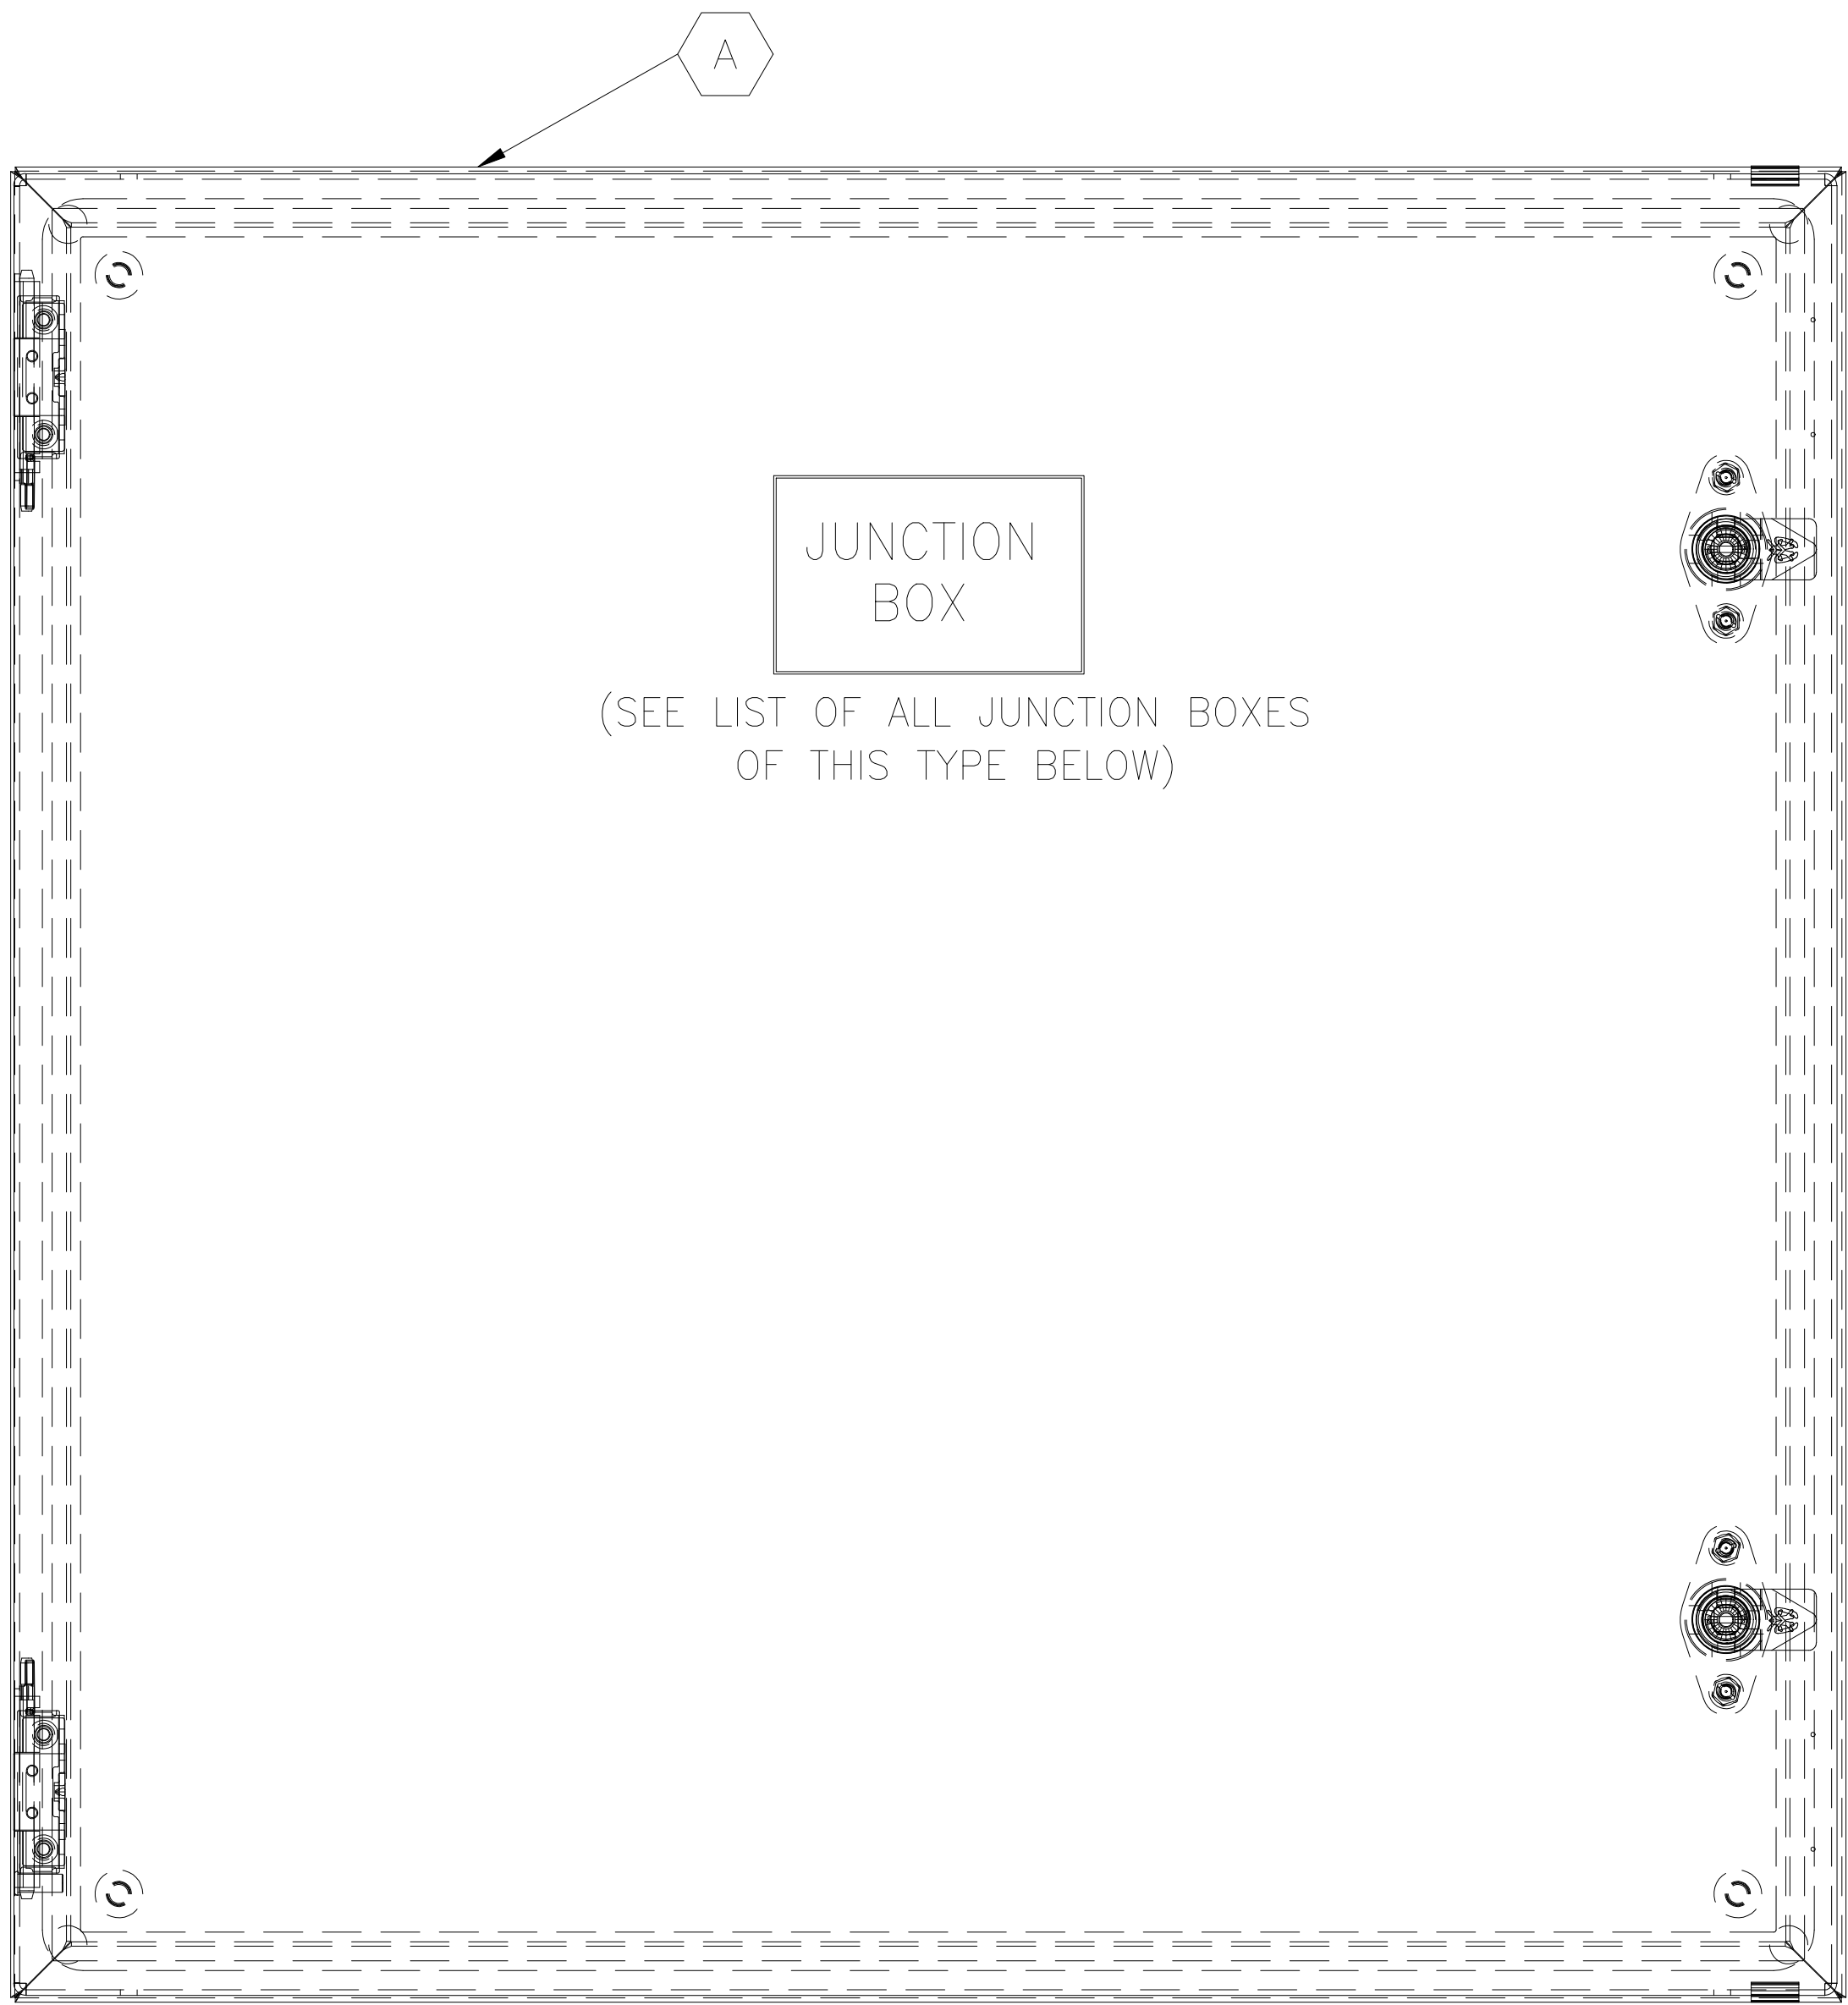

- NOTES:
1. ALL JUNCTION BOXES SHALL BE BONDD TO ALL EQUIPMENT GROUNDING CONDUCTORS PASSING THROUGH THE BOX.
 2. ALL CONDUIT, TRAY AND INTERMEDIATE BOXES SHALL BE CONTINUOUS WITH BONDING JUMPERS PROVIDED AS NEEDED TO MEET THIS REQUIREMENT. IN NO CASE SHALL THE CONDUIT OR TRAY BE CONSIDERED AN EQUIPMENT GROUNDING CONDUCTOR.
 3. SEE GROUNDING DETAIL DRAWING 230927-E-605 FOR DETAILS FOR BONDING ALL BOXES.

TB1	
01	
02	
03	
04	
05	
06	
07	
08	
09	
10	
11	
12	
13	
14	
15	
16	
17	
18	
19	
20	
21	
22	
23	
24	
25	
26	
27	
28	
29	
30	
31	
32	
33	
34	
35	

TB2	
PR-01	
PR-01	
SHIELD	
PR-02	
PR-02	
SHIELD	
PR-03	
PR-03	
SHIELD	
PR-04	
PR-04	
SHIELD	
PR-05	
PR-05	
SHIELD	
PR-06	
PR-06	
SHIELD	
PR-07	
PR-07	
SHIELD	
PR-08	
PR-08	
SHIELD	
PR-09	
PR-09	
SHIELD	
PR-10	
PR-10	
SHIELD	
PR-11	
PR-11	
SHIELD	
PR-12	
PR-12	
SHIELD	
SPARE	
SPARE	
SPARE	
SPARE	

LETTER	DESCRIPTION	MANUFACTURER	PART NO.	QUANTITY
A	NEMA 4X ENCLOSURE, 24"x16"x8"	HOFFMAN	CSD241610SS	1
B	BACKPANEL, 22.2" X 12.2"	HOFFMAN	CP2416	1
C	TERMINAL BLOCK, FINGER-SAFE, HIGH DENSITY	ALLEN-BRADLEY	1492-J3	75
F	END ANCHORS	ALLEN-BRADLEY	1492-EAJ35	4
G	END BARRIER	ALLEN-BRADLEY	1492-EBJ3	2
H	35mm MOUNTING RAIL	ALLEN-BRADLEY	199-DR1	AS REQ'D
K	WIRING DUCT, WHITE, WITH COVER - SIZE AS SHOWN	PANDUIT	TYPE "NE"	AS REQ'D

JUNCTION BOXES
1611BC03.JB1
1631FM01.JB1
1631GD01.JB1
1631WI01.JB1
1651LQ31.JB1

ISSUED FOR
CONSTRUCTION
DATE: 240CT24 BY: JK PHIPPS

2	07JUL25	REISED PER CLIENT COMMENTS	SAB	JKP	JKP
1	03APR25	REVISED LIST OF JUNCTION BOX TAGS	SAB	JKP	JKP
0	240CT24	ISSUED FOR CONSTRUCTION	SAB	JKP	JKP
REV.	DATE	DESCRIPTION	BY	CHKD.	APPR.


PENTA
PENTA Engineering Co. LLC
10123 Corporate Square Drive, St. Louis, MO 63132-2905
www.penta.net; Phone: 314-878-0123; Fax: 314-878-0120

This drawing and the information contained herein is submitted confidentially and is the property of Penta Engineering Co. LLC. It may not be duplicated, disclosed, or utilized without written consent from Penta Engineering Co. LLC.

FINISH MILL AREA
LEAMINGTON, UTAH
ELECTRICAL



24x16 JUNCTION BOX DETAIL

DESIGNED: Bahr	DATE: 16APR24	PENTA DRAWING NUMBER	REV.
DRAWN: Bahr	DATE: 16APR24	230927-E-611	2
CHECKED: PHIPPS	DATE: 240CT24	CLIENT DRAWING NUMBER	
APPROVED: PHIPPS	SCALE: 6"=1'-0"		

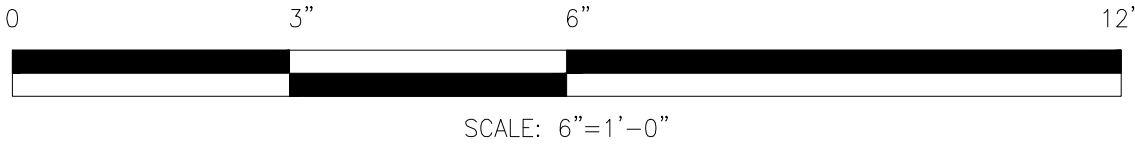

SCALE: 6"=1'-0"


T:\Loesche\20230927-Leamington\Elec\Current Dwg\230927-E-611.dwg

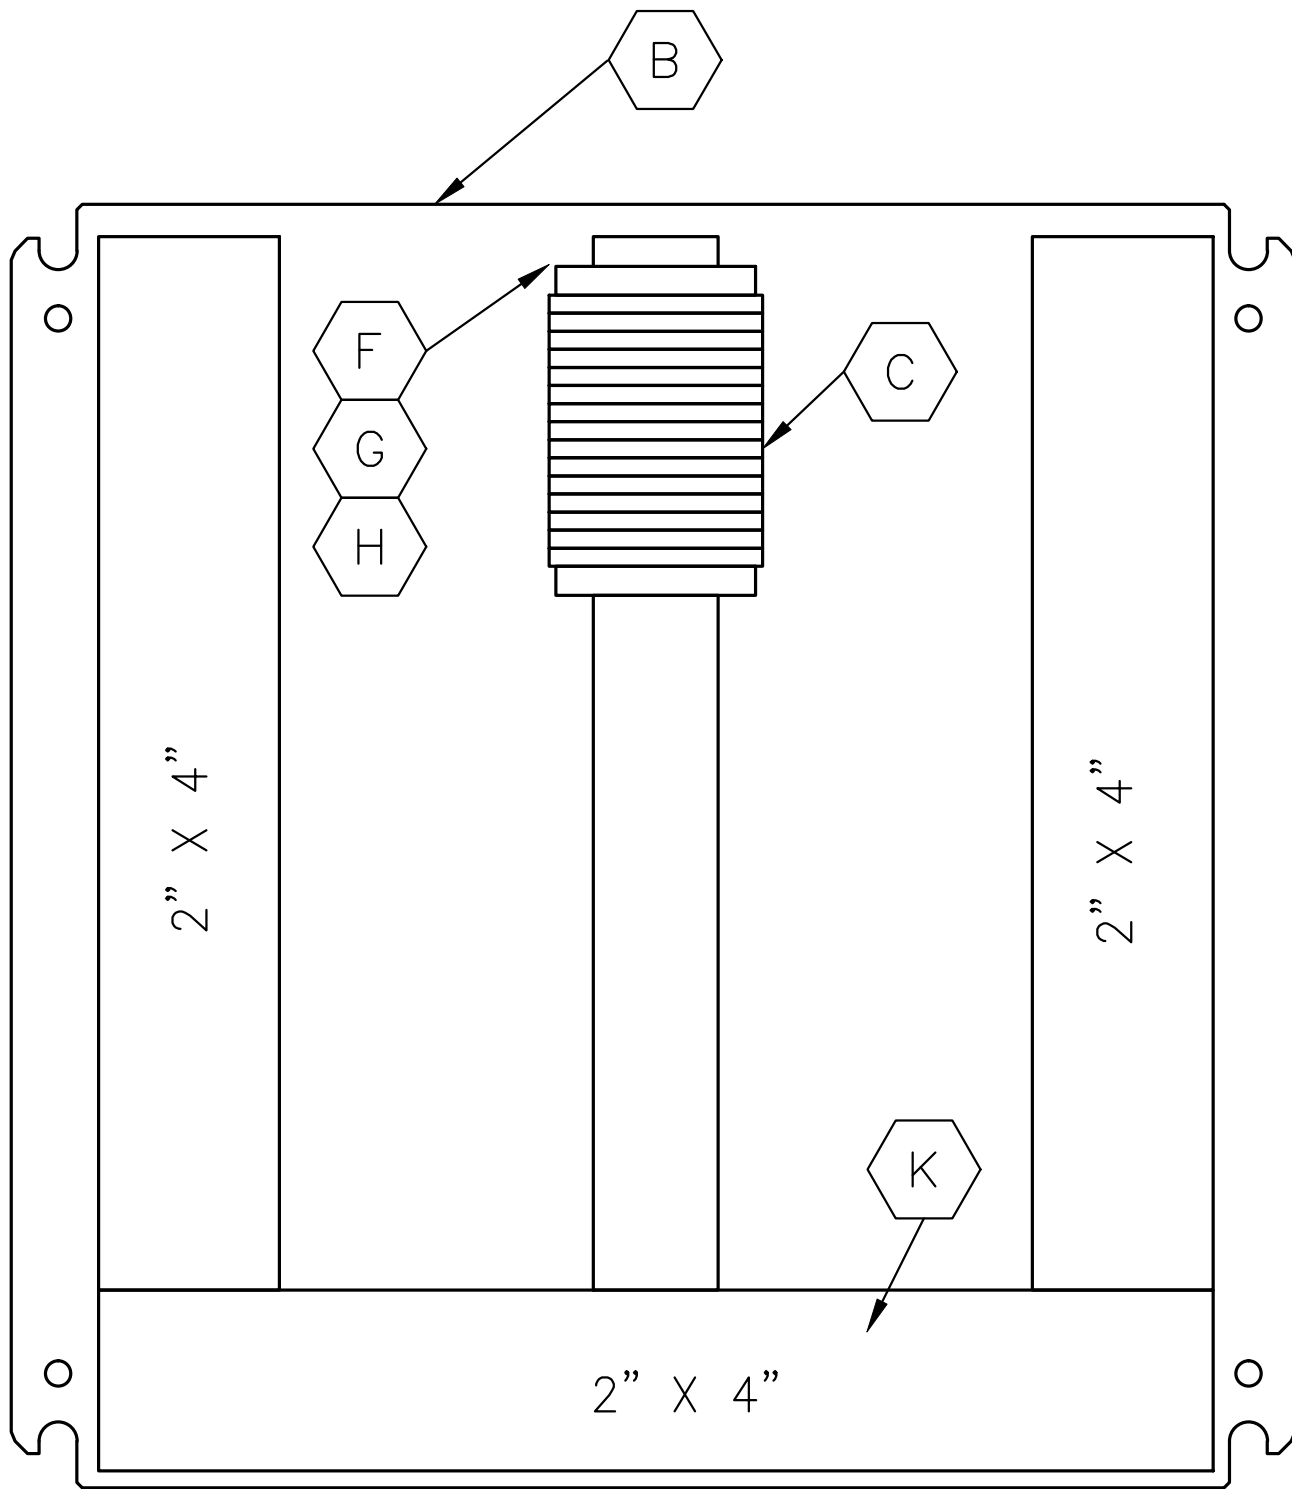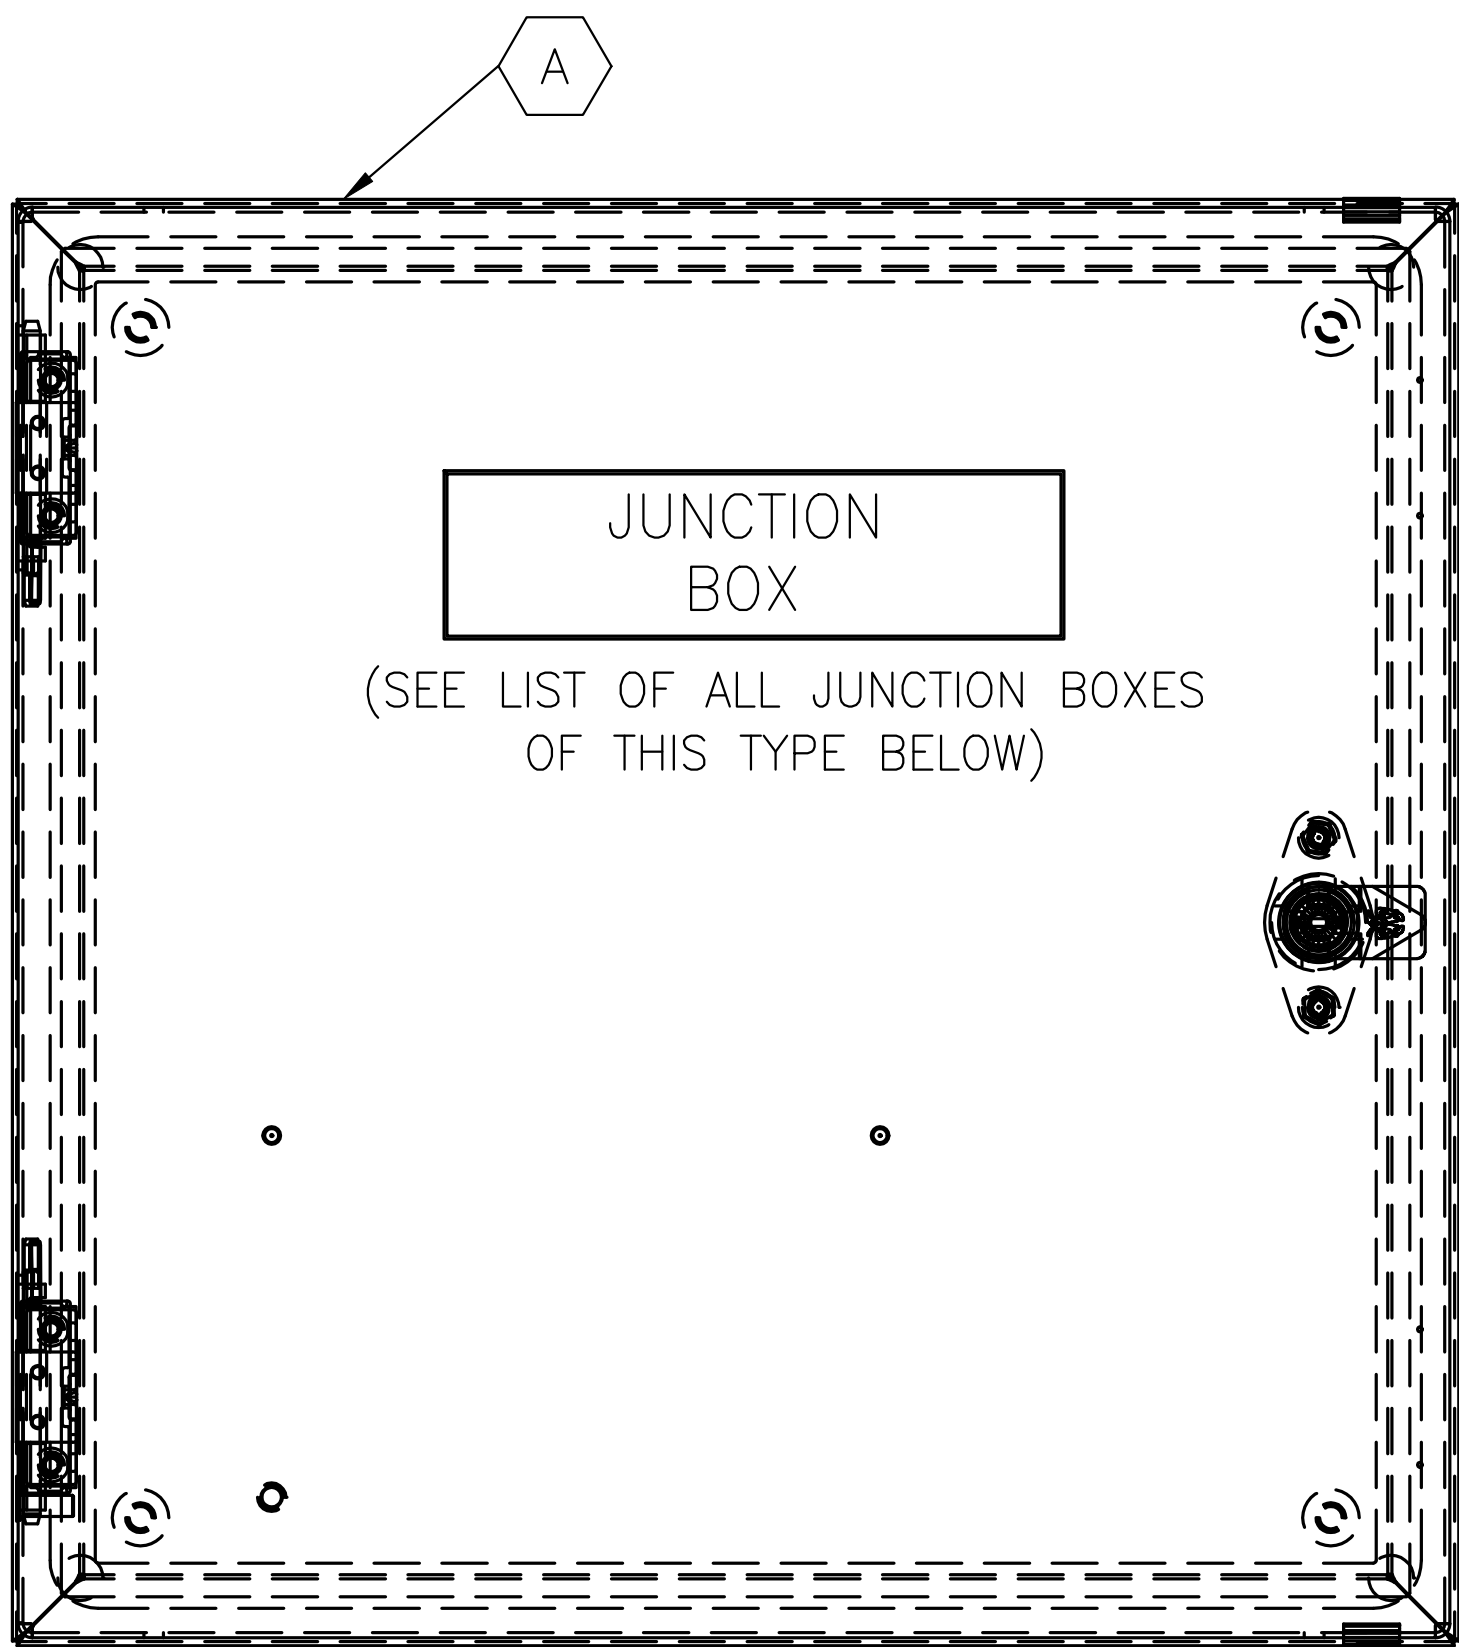

TB	
	01
	02
	03
	04
	05
	06
	07
	08
	09
	10
	11
	12
	13
	14
	15

LETTER	DESCRIPTION	MANUFACTURER	PART NO.	QUANTITY
A	NEMA 4X ENCLOSURE, 12"x12"x6"	HOFFMAN	CSD1212SS	1
B	BACKPANEL, 10.2" X 10.2"	HOFFMAN	CP1212	1
C	TERMINAL BLOCK, FINGER-SAFE, HIGH DENSITY	ALLEN-BRADLEY	1492-J3	15
F	END ANCHORS	ALLEN-BRADLEY	1492-EAJ35	~2
G	END BARRIER	ALLEN-BRADLEY	1492-EBJ3	~1
H	35mm MOUNTING RAIL	ALLEN-BRADLEY	199-DR1	AS REQ'D
K	WIRING DUCT, WHITE, WITH COVER - SIZE AS SHOWN	PANDUIT	TYPE "NE"	AS REQ'D

JUNCTION BOXES		
1621DG01.JB1	1661FN01.JB1	JB-HW-INTL
1631GB01.JB1	1661FN21.JB1	
1641BC01.JB1	1661HG01.JB1	
1641DG01.JB1	1681AS01.JB1	
1651AS01.JB1	1681AS02.JB1	
1651AS02.JB1	1681DG10.JB1	
1651CL01.JB1		
1651DU01.JB1		
1651RG01.JB1		
1651RG02.JB1		
1651SG01.JB1		
1651SG02.JB1		
1661DU01.JB1		
1661DU02.JB1		
1661DU04.JB1		

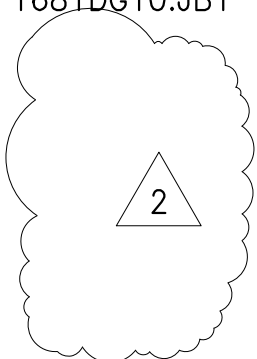

- NOTES:
1. ALL JUNCTION BOXES SHALL BE BONDED TO ALL EQUIPMENT GROUNDING CONDUCTORS PASSING THROUGH THE BOX.
 2. ALL CONDUIT, TRAY AND INTERMEDIATE BOXES SHALL BE CONTINUOUS WITH BONDING JUMPERS PROVIDED AS NEEDED TO MEET THIS REQUIREMENT. IN NO CASE SHALL THE CONDUIT OR TRAY BE CONSIDERED AN EQUIPMENT GROUNDING CONDUCTOR.
 3. SEE GROUNDING DETAIL DRAWING 230927-E-605 FOR DETAILS FOR BONDING ALL BOXES.


ISSUED FOR
CONSTRUCTION
DATE: 24OCT24 BY: JK PHIPPS




PENTA Engineering Co. LLC
10123 Corporate Square Drive, St. Louis, MO 63132-2905
www.penta.net; Phone: 314-878-0123; Fax: 314-878-0120

This drawing and the information contained herein is submitted confidentially and is the property of Penta Engineering Co. LLC. It may not be duplicated, disclosed, or utilized without written consent from Penta Engineering Co. LLC.

A GRM COMPANY

FINISH MILL AREA LEAMINGTON, UTAH ELECTRICAL 12 x12 JUNCTION BOX DETAIL			
DESIGNED: BAHR	DATE: 16APR24	PENTA DRAWING NUMBER	REV.
DRAWN: BAHR	DATE: 16APR24	230927-E-608	2
CHECKED: PHIPPS	DATE: 24OCT24	CLIENT DRAWING NUMBER	
APPROVED: PHIPPS	SCALE: 6"=1'-0"		

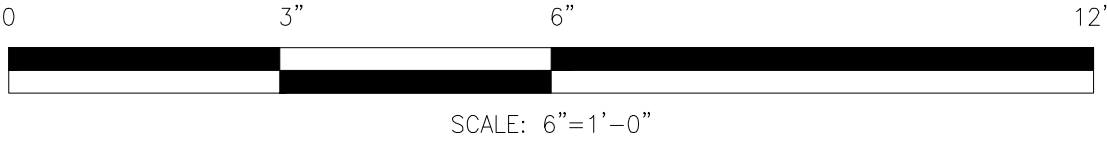

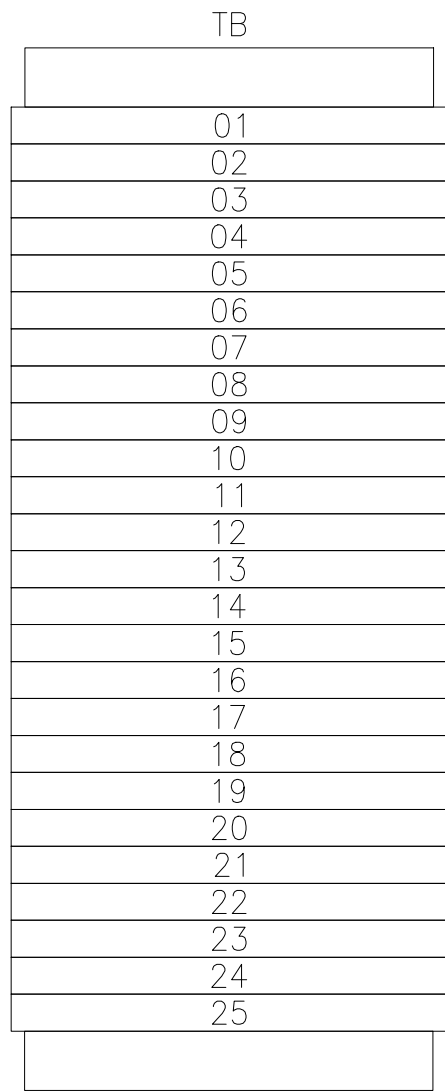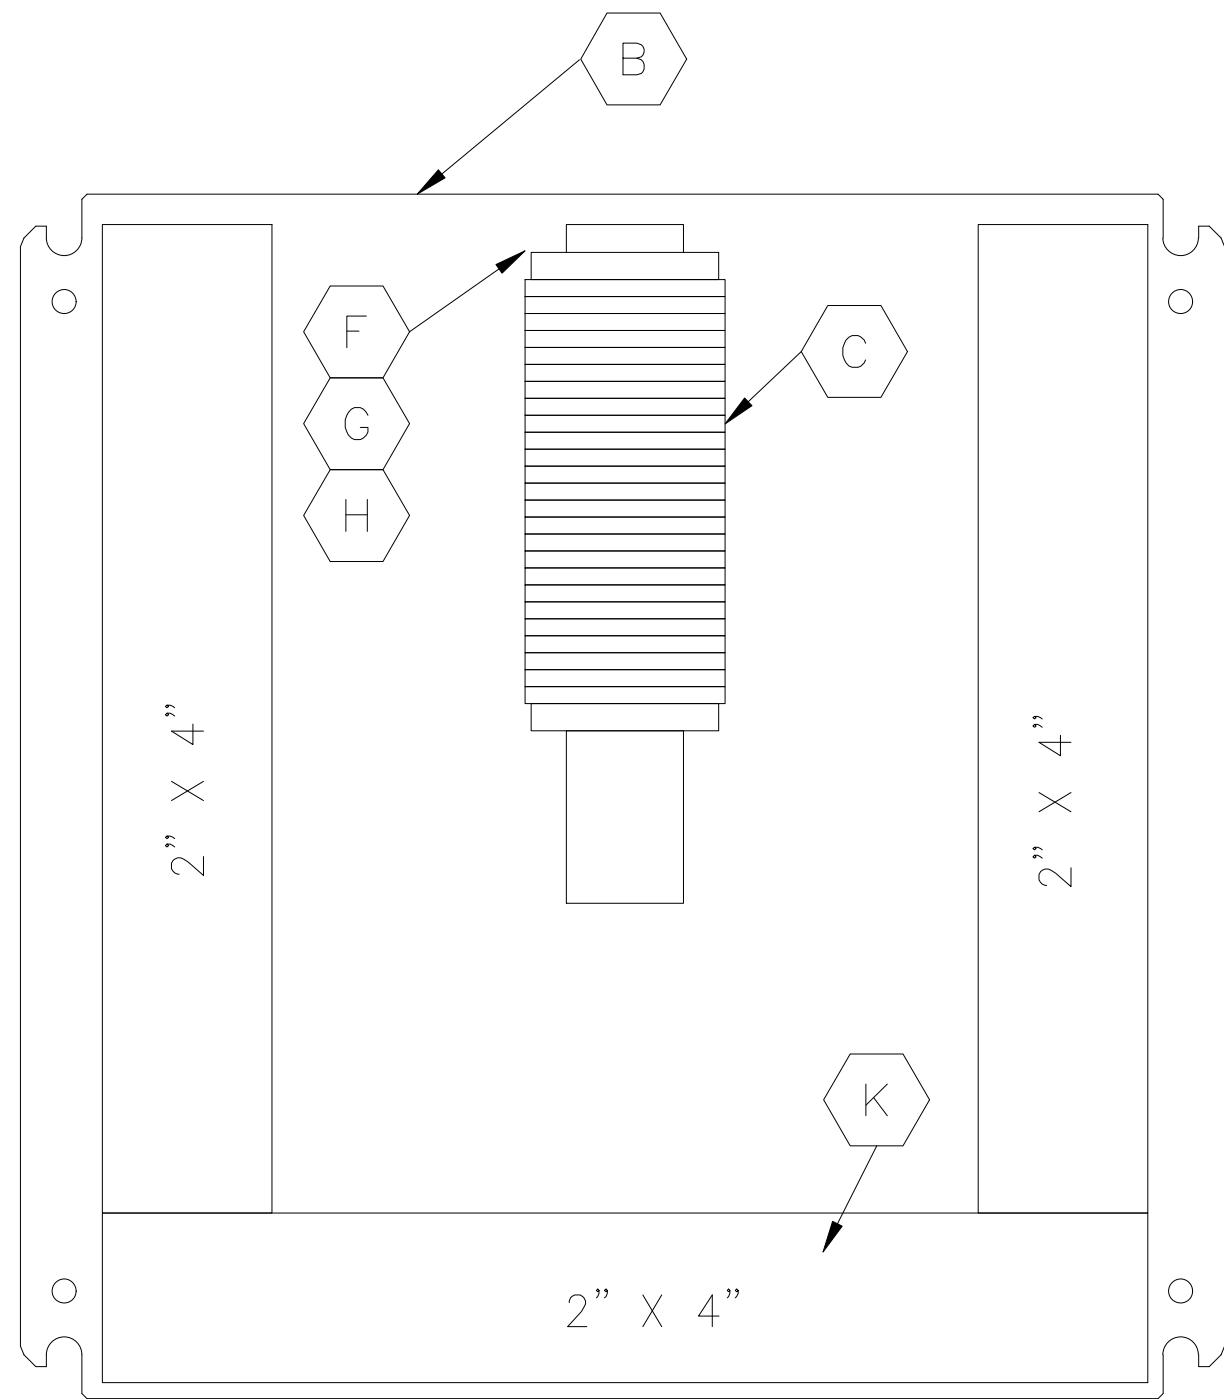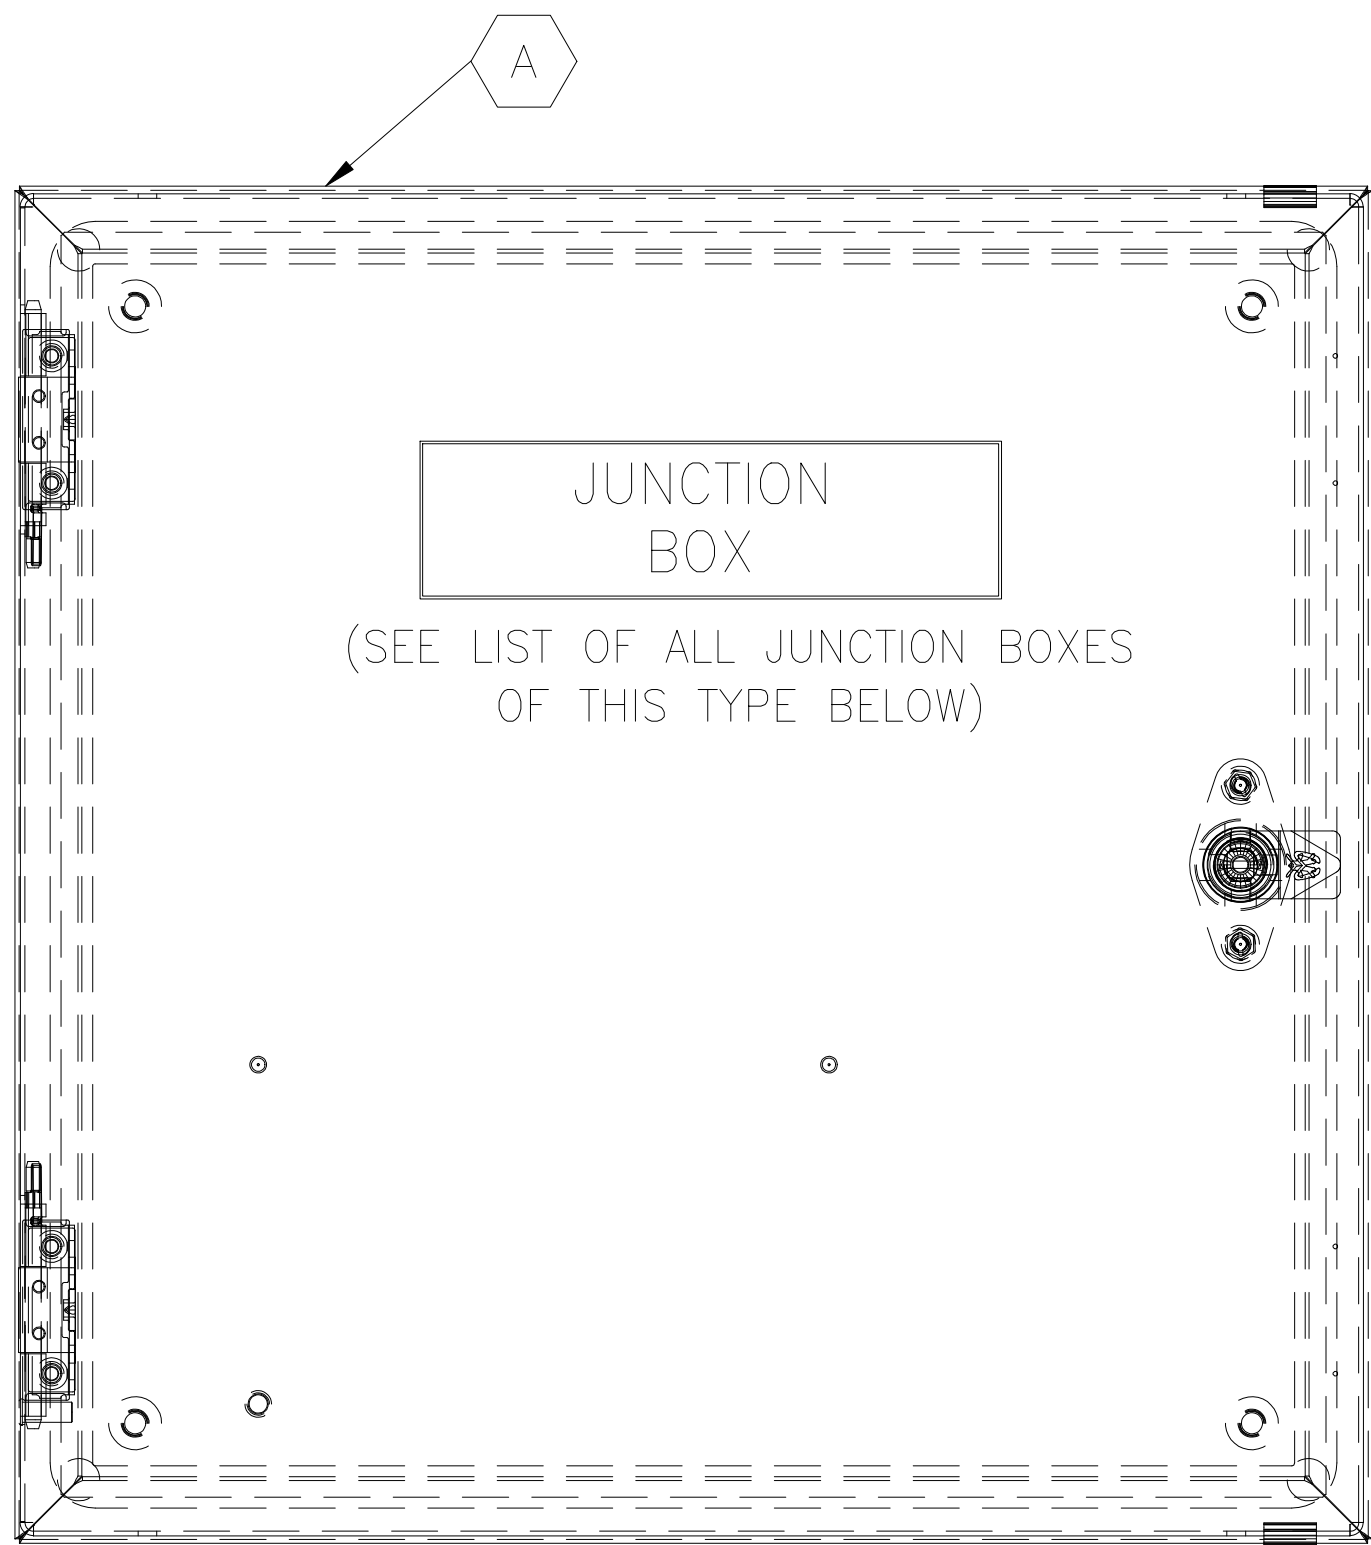

- NOTES:
1. ALL JUNCTION BOXES SHALL BE BONDD TO ALL EQUIPMENT GROUNDING CONDUCTORS PASSING THROUGH THE BOX.
 2. ALL CONDUIT, TRAY AND INTERMEDIATE BOXES SHALL BE CONTINUOUS WITH BONDING JUMPERS PROVIDED AS NEEDED TO MEET THIS REQUIREMENT. IN NO CASE SHALL THE CONDUIT OR TRAY BE CONSIDERED AN EQUIPMENT GROUNDING CONDUCTOR.
 3. SEE GROUNDING DETAIL DRAWING 230927-E-605 FOR DETAILS FOR BONDING ALL BOXES.

LETTER	DESCRIPTION	MANUFACTURER	PART NO.	QUANTITY
A	NEMA 4X ENCLOSURE, 12"x12"x6"	HOFFMAN	CSD1212SS	1
B	BACKPANEL, 10.2" X 10.2"	HOFFMAN	CP1212	1
C	TERMINAL BLOCK, FINGER-SAFE, HIGH DENSITY	ALLEN-BRADLEY	1492-J3	25
F	END ANCHORS	ALLEN-BRADLEY	1492-EAJ35	~2
G	END BARRIER	ALLEN-BRADLEY	1492-EBJ3	~1
H	35mm MOUNTING RAIL	ALLEN-BRADLEY	199-DR1	AS REQ'D
K	WIRING DUCT, WHITE, WITH COVER - SIZE AS SHOWN	PANDUIT	TYPE "NE"	AS REQ'D

JUNCTION BOXES
1611BC01.JB1
1611BC05.JB1
1621BC01.JB2
1621BC02.JB2
1621MS01.JB1
1631HS11.JB1
1631LQ41.JB1
1631MD01.JB1
1631RF01.JB1
1641BC01.JB2
1641MS01.JB1
1651BF01.JB1
1651LQ42.JB1
1661SG01.JB1
1681BE01.JB1
1681CQ01.JB1
1681DE01.JB1

ISSUED FOR
CONSTRUCTION
DATE: 240CT24 BY: JK PHIPPS

REV.	DATE	DESCRIPTION	BY	CHKD.	APPR.
2	07JUL25	REVISED PER CLIENT COMMENTS	SAB	JKP	JKP
1	03APR25	REVISED LIST OF JUNCTION BOX TAGS	SAB	JKP	JKP
0	240CT24	ISSUED FOR CONSTRUCTION	SAB	JKP	JKP



PENTA
PENTA Engineering Co. LLC
10123 Corporate Square Drive, St. Louis, MO 63132-2905
www.penta.net | Phone: 314-878-0123 | Fax: 314-878-0120

This drawing and the information contained herein is submitted confidentially and is the property of Penta Engineering Co. LLC. It may not be duplicated, disclosed, or utilized without written consent from Penta Engineering Co. LLC.



FINISH MILL AREA
LEAMINGTON, UTAH
ELECTRICAL

12x12 JUNCTION BOX DETAIL

DESIGNED: Bahr	DATE: 16APR24	PENTA DRAWING NUMBER	REV.
DRAWN: Bahr	DATE: 16APR24	230927-E-609	2
CHECKED: PHIPPS	DATE: 240CT24	CLIENT DRAWING NUMBER	
APPROVED: PHIPPS	SCALE: 6"=1'-0"		

